
벽면 이용 간판 도면 「다시 수선」 (가상 상호) 정면·측면·단면

도면번호 SG-01/01 (도면 1장) | 단위 mm | 축척: 정면도·측면도 1:25, 간판면 1:21, 단면 1:2
작성일 2026-11 | 작성: 응모자(성명은 신청서 1절에 기재) | 기준 지자체: 미지정(조례 확인 필요)

정면도 (건물 입면, 칸 2) 1:25

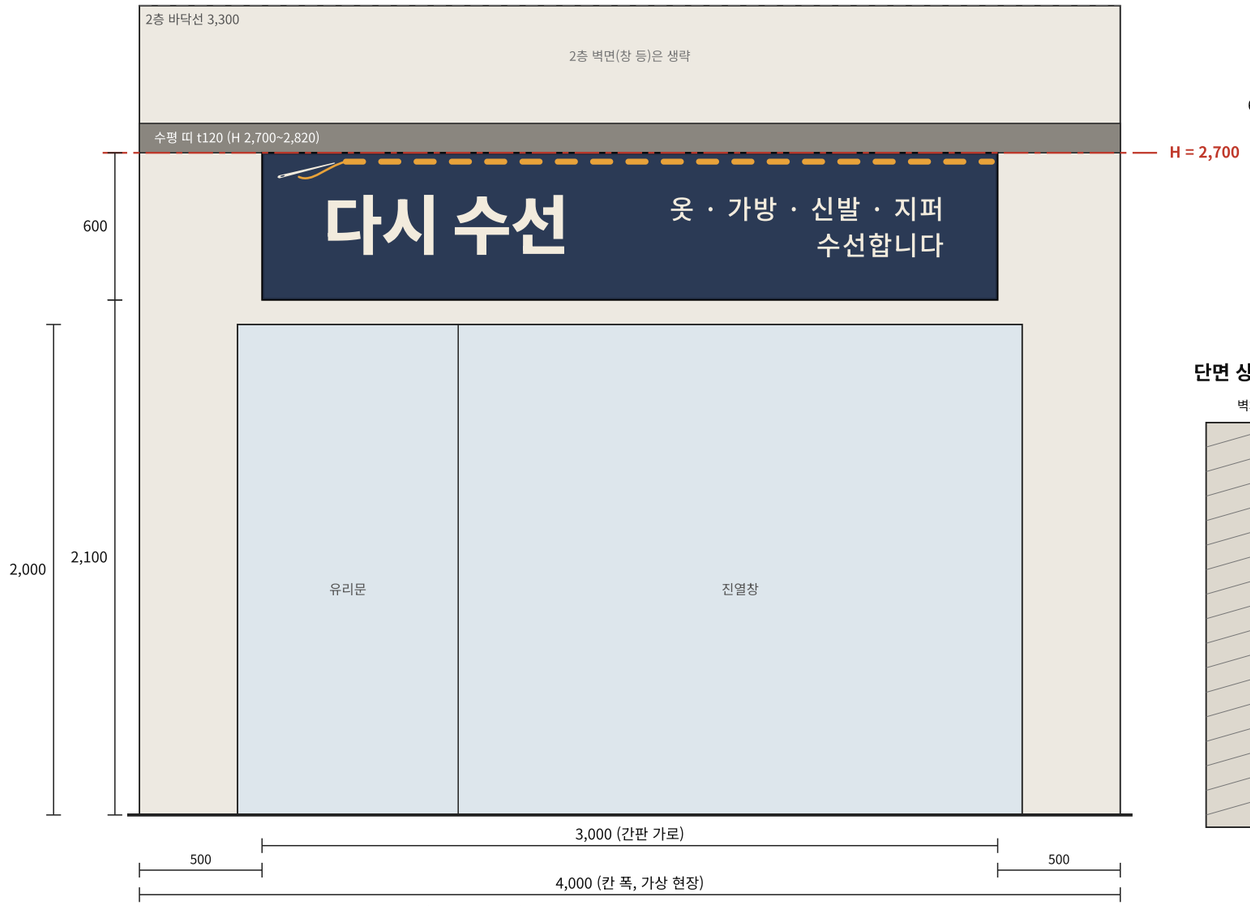

이웃 간판 윗변은 H보다 과일가게 +250, 국숫집 -220 (가상 현장 가정값).
이웃 벽면에는 선·표시를 하지 않는다.
치수 2,100 = 간판 아랫변 높이, 2,000 = 개구부 윗선 높이.
H = 띠 아랫선 = 간판 윗변.


간판면 정면 1:21 (판 3,000 x 600)




박음질 중심선 = 판 윗변 아래 36 (H-36). 판 윗변 = H. 상호 글자 262, 업종 문구 약 107(원 74 x 1.45).
슬릿 24 x 94(직선 70 + 둥근 끝) 피치 144, 19개. #E8A23A는 주간 색이며 야간에는 슬릿 뒤 LED 2,700K가 비친다.
글자 4개(다 시 수 선): 입체 리버스 채널. 업종 문구 2줄: 컷팅 시트. 모든 글자는 한글이다.

측면도 1:25

돌출 87 (단면 상세 참조)

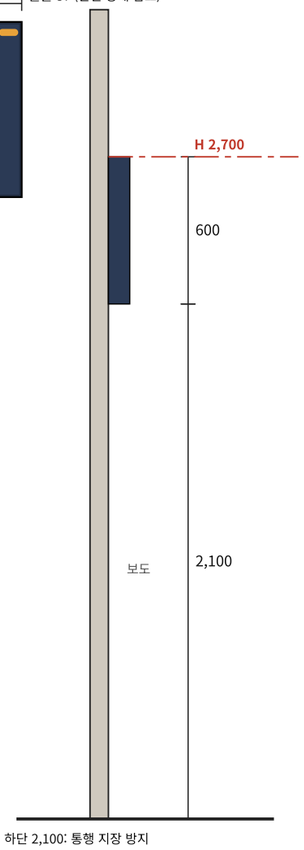

단면 상세 (판 윗변부, 수직 단면) 1:2

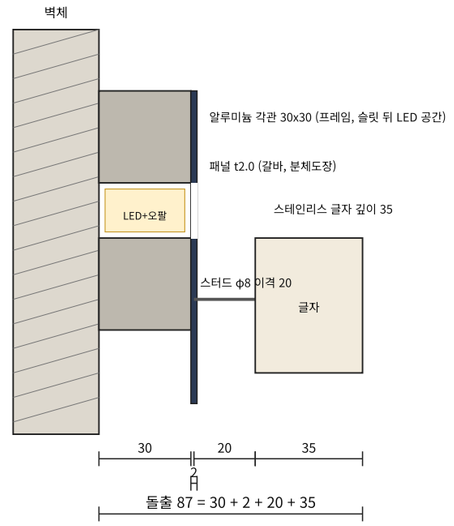

소재·재질

부위	재질·사양	수량
패널	갈바(아연도금)강판 t2.0, 무광 분체도장 #2B3A55	3,000x600 1장
후면 프레임	알루미늄 각관 30x30 t1.5, 흑색 아노다이징. 외곽 + 수직 보강 3개(간격 750). 슬릿 뒤에 LED 띠와 오팔 아크릴 3t	1식
상호 글자	스테인리스 304 t1.2 채널 글자, 깊이 35, 상아 #F2EBDD 분체도장, 리버스(후광) 방식, 스터드 φ8 로 패널에서 20 띄움	4개
업종 문구	옥외용 컷팅 시트 상아 #F2EBDD, 패널 직접 부착, 원 크기 74 x 1.45 = 약 107	2줄
박음질 슬릿	레이저 절단 폭 24, 길이 94(둥근 끝), 피치 144. 중심선 판 윗변 아래 36. 뒤에 오팔 아크릴 3t	19개
고정	케미컬 앵커 M8, 벽체 재질 확인 후 확정(설계 값)	8점
중량(개산, 설계값)	강판 28.3 + 프레임 4.1 + 글자 3 + 조명·부속 약 4 = 약 40kg	-

색채 (HEX)

명칭		HEX	사용처
패널 인디고		#2B3A55	판 전체, 무광
테두리선		#1F2A3E	판 안쪽 6mm 선
상아		#F2EBDD	상호·업종 문구·바늘
머스터드		#E8A23A	박음질 슬릿(주간)
조명 광색 2,700K		#FFC46B	야간 슬릿·후광
건물 수평 띠(기존, 가상)		#8A867F	H 기준선, 변경 없음

형광·야광 계열 색은 쓰지 않는다. 일반 분체도장·컷팅 시트 기준.

조명 사양

항목	사양
방식	글자 후광(리버스 채널) + 박음질 슬릿 후면 확산. 광원 외부 비노출
광원	LED 2,700K, 연색성 Ra 80 이상(설계 값)
점멸·변화	점멸 없음, 색 변화 없음, 동영상 없음
밝기	야간 300 cd/㎡ 이하 목표(설계 목표, 법정 기준 아님). 조례 기준 확인 필요
전력	정격 총 40W 이하(설계 값), DC 12V 전원장치 1대 판 뒤 설치
전기	안전인증 자재, 배선 외부 비노출, 전기공사업법에 맞는 시공(영 제14조제1항)
점등	일몰 후 영업 종료까지, 조도 센서 + 타이머(설계 값)

법규 적합 요약 (전체 22항목 법규 체크표는 공모신청서 3-4에 있다. 도면은 규격에 따라 1장)

항목	근거 조항	설계 대응	판정
종류	영 제3조제1호가목	벽면 이용 간판	분류
허가 대상 요건	영 제4조제1항제1호	한 변 3.0m, 1층, 자사 상호	비해당(문언 기준)
신고 대상 요건	영 제5조제1항제1호	1.80㎡, 1층	비해당(면적 산정 방법 확인 필요)
한글 표기	영 제12조제2항	상호·업종 전부 한글	충족 설계
통행·낙하	영 제12조제5항	하단 2,100, 돌출 87, 앵커 8점	충족 설계(벽체 확인 필요)
형광·야광	영 제12조제6항	일반 분체도장·시트	충족 설계
고정·수량	영 제12조제7항·제8항	벽체 고정, 간판 1개	충족 설계(수량 상한은 조례)
광원·전기	영 제14조제1항~제3항	LED 비노출, 점멸 없음	충족 설계(밝기·색깔은 조례)
조례 위임	영 제12조제9항 등	규격·돌출·층·밝기·명판·표시기간	**확인 필요**(기준 지자체 미지정)

비고

- 설계 값(2,100 / 87 / 앵커 8점 / 300 cd/㎡ / 40W 등)은 법정 수치가 아닌 이 작품의 설계 값이다.
- 건물 수평 띠(H 2,700~2,820)·칸 폭 4,000·이웃 간판 높이는 가상 현장 가정값이다. 실제 현장이면 실측으로 교체한다.
- 박음질 슬릿은 자기 판 안쪽에서만 끝난다. 이웃 벽면에는 어떤 표시도 하지 않는다.
- "충족 설계"는 조항 문언에 비춘 설계자 판단이며 인허가 결정이 아니다. "확인 필요"는 원문을 열람하지 못한 항목이다. 조항 요지는 응모자가 제출 전 국가법령정보센터 원문과 대조한다.
- 글꼴 Noto Sans KR(SIL OFL 1.1), 상호 글자는 윤곽선. 상호 "다시 수선"은 가상이며 상표 선행 검색은 응모자가 확인한다.